


1. 평면도 (외벽 Y2 ~ 양생굴 15·16 내부) S=1:100

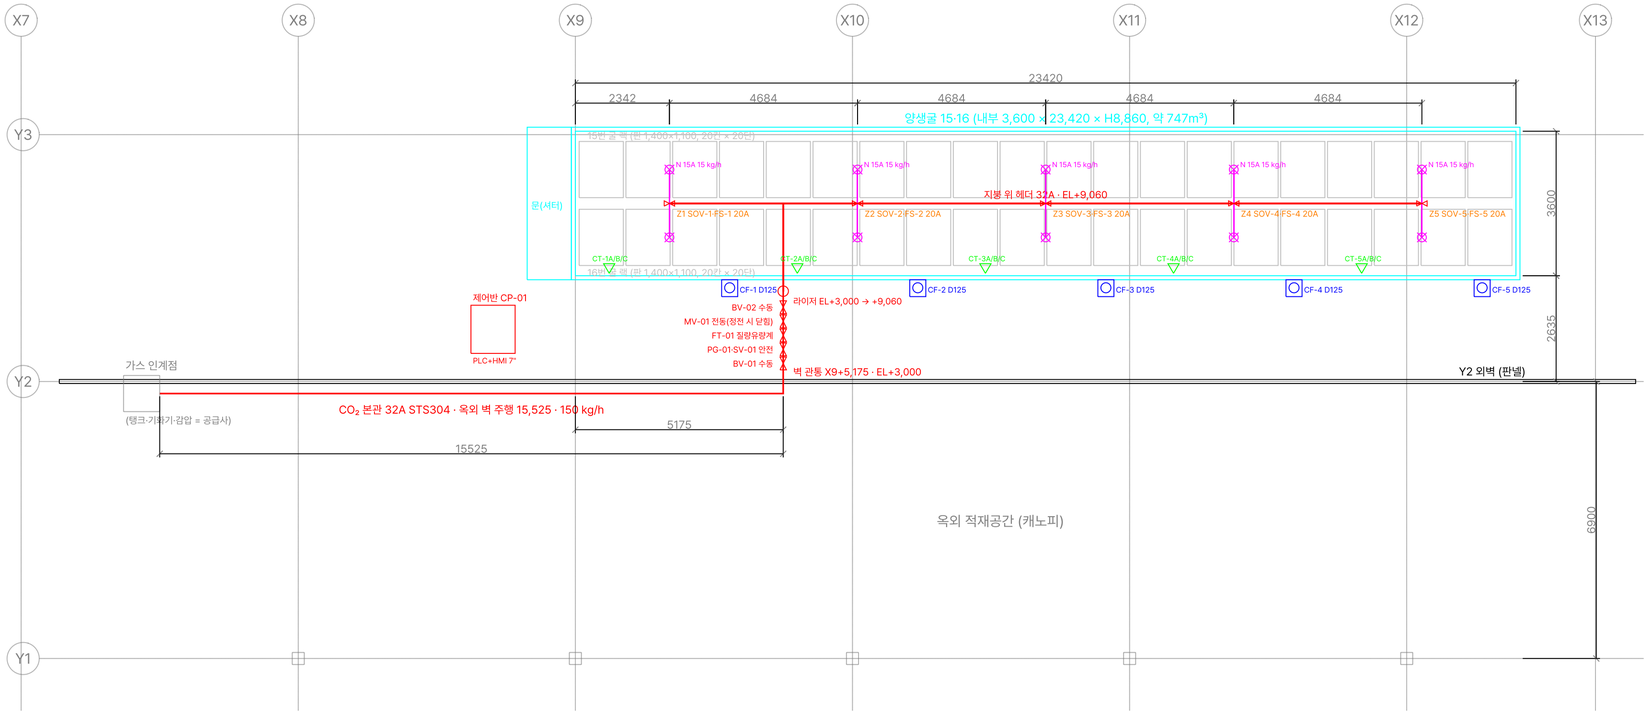

2. 횡단면도 (CO_2 인입부 · 구간 분기) S=1:100

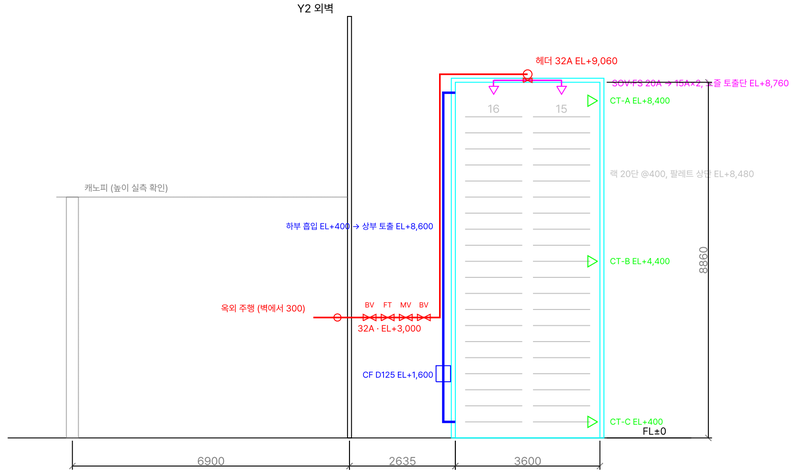

3. CO_2 공급 계통도 · 설계 유량 (N.T.S)

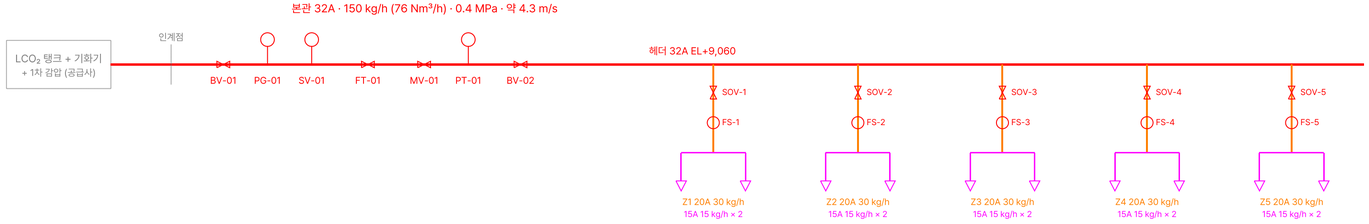

4. 설계 유량표 (초안 · 가정값, 상세설계 때 확정)

구간	관경	유량 kg/h	Nm³/h	유속 m/s	비고
본관·헤더	32A	150	76	4.3	초기 충전 2시간 기준 (747m³ → 20%)
구간 분기 ×5	20A	30	15	2.2	SOV + 플로우 스위치
노즐 지관 ×10	15A	15	7.6	1.9	노즐 오리피스 D2.2 상당
유지 운전	32A	최대 26	13	0.8	누설 시간당 2% 기준 보충

주) 1. 좌표: X = X9 통심 기준, Y = Y2 통심 기준, EL = FL±0. 건물·랙 치수는 발주처 참고도면(DWG), 배관 위치는 견적요청서 20260916L-B01 기준.
2. 유량·유속은 감압 후 0.4 MPa, 20°C, STS304 Sch10S 내경 기준 계산값. CO_2 20% · 18시간 유지, 블록 흡수량은 시운전 때 측정해 보정.
3. 구간 5개(Z1~Z5) 각 구간 CO_2 센서 3점(상·중·하) 총 15점, 순환 덕트팬 D125 5세트. 기존 설비 위치는 착수 전 실측으로 확정.
4. 범례: 빨강 CO_2 32A / 주황 20A / 자홍 15A / 파랑 순환 덕트 D125 / 초록 CO_2 센서 / 회색 점선 = 가스 공급사 범위.

엔엠솔루션 · 데코페이브 양생굴 15·16 CO_2 배관 설계도 (초안 v1)
도면번호 NM-DWG-2611-01 · 2026-11-14 · 단위 mm
검토용 초안 — 시공상세도 아님