


1. 평면도 (외벽 Y2 ~ 양생굴 15·16 내부) S=1:100

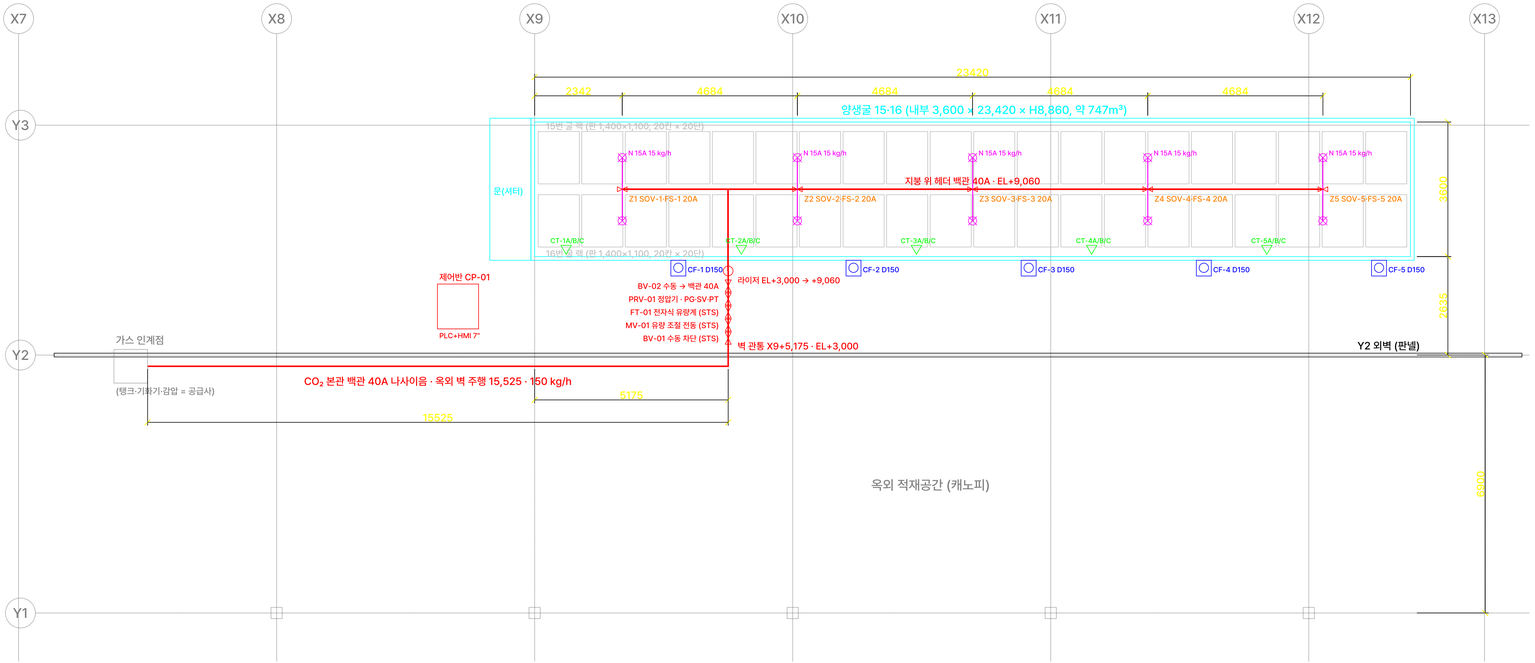

2. 횡단면도 (CO_2 인입부 · 구간 분기) S=1:100

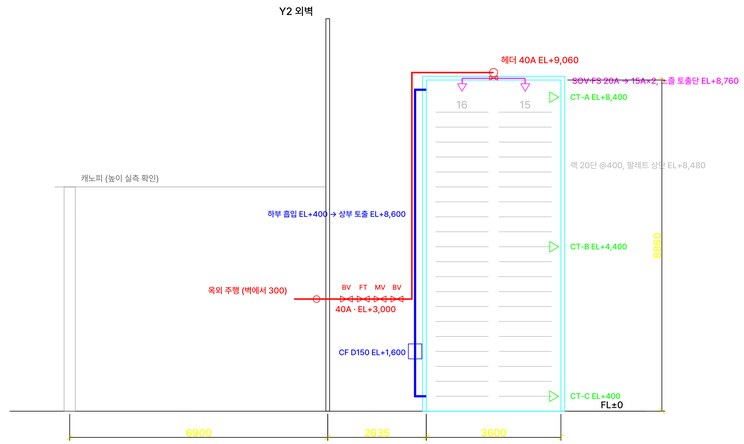

3. CO_2 공급 계통도 · 설계 유량 (N.T.S)

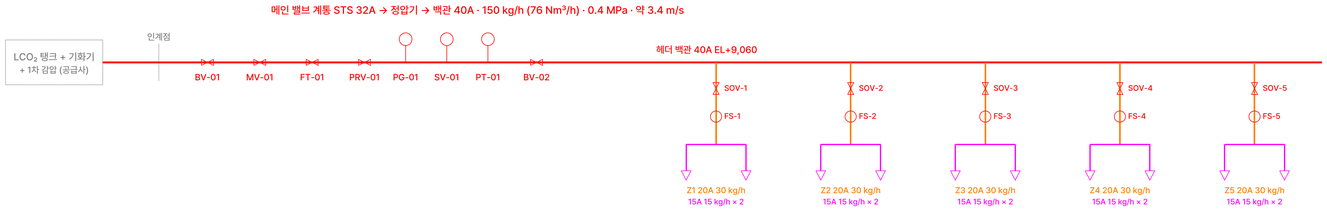

4. 설계 유량표 (체적 기준 · 상세설계 때 확정)

구간	관경	유량 kg/h	Nm³/h	유속 m/s	비고
본관-헤더	40A	150	76	3.4	초기 충전 2시간 기준 (747m³ → 20%), 백관 나사이음
구간 분기 ×5	20A	30	15	2.2	SOV + 플로우 스위치
노즐 지관 ×10	15A	15	7.6	1.9	노즐 오리피스 D2.2 상당
유지 운전	40A	최대 26	13	0.6	누설 시간당 2% 기준, MV-01 개도로 보충

주) 1. 좌표: X = X9 통심 기준, Y = Y2 통심 기준, EL = FL±0. 건물·랙 치수는 발주처 참고도면(DWG), 배관 위치는 견적요청서 20260916L-B01 기준.
2. 유량·유속은 정압기 2차 0.4 MPa(가정), 20°C 계산값. 체적 기준(CO_2 20% · 18시간 유지). 블록 흡수량 기준이면 다시 계산.
3. 구간 5개(Z1~Z5) 각 구간 CO_2 센서 3점(상·중·하) 총 15점, 순환 덕트팬 D150 5세트. 기존 설비 위치는 착수 전 실측으로 확정.
4. 범례: 빨강 CO_2 본관 백관 40A(밸브 계통 STS 32A) / 주황 20A 백관 / 자홍 15A STS / 파랑 순환 덕트 / 초록 CO_2 센서 / 회색 점선 = 가스 공급사 범위.

엔엠솔루션 · 데코페이브 양생굴 15·16 CO_2 배관 설계도 (v2)
도면번호 NM-DWG-2611-01 · 2026-11-14 · 단위 mm
검토용 초안 — 시공상세도 아님